

WINSTON ORTA SEHPA — MONTAJ (tablanın ALTINDAN bakış) · tabla 18 meşe + 2 kat 18 MDF şerit = 54 mm kenar · şerit 65 mm

1. KAT (tablanın hemen altına)

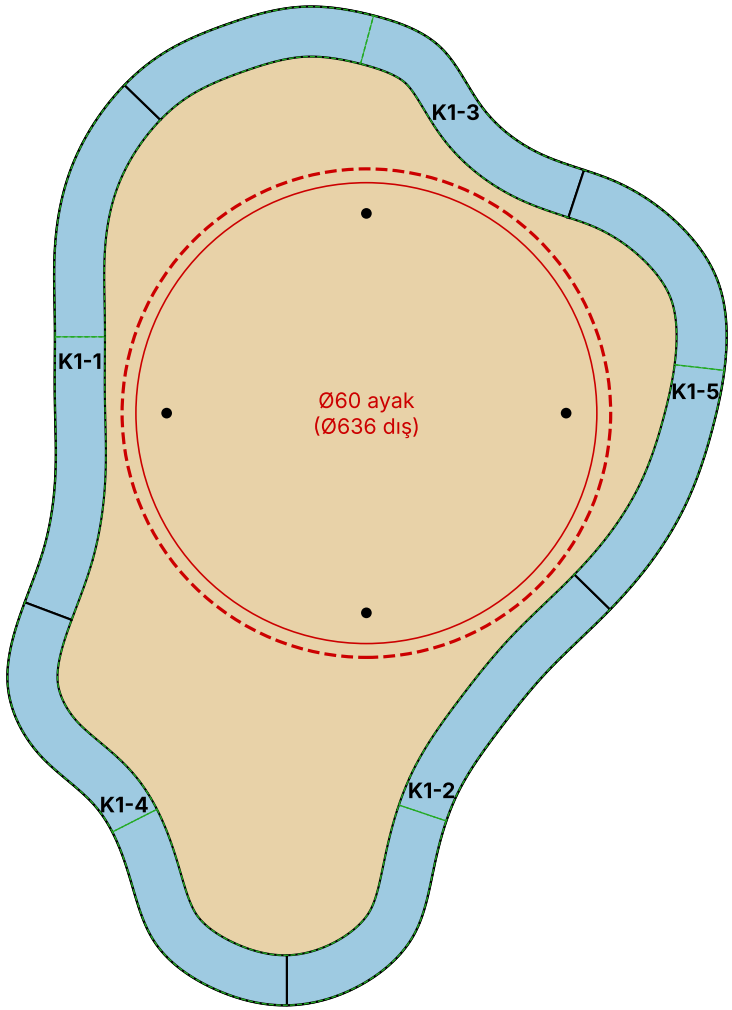


2. KAT (1. katın üstüne, ekler kaydırılmış)

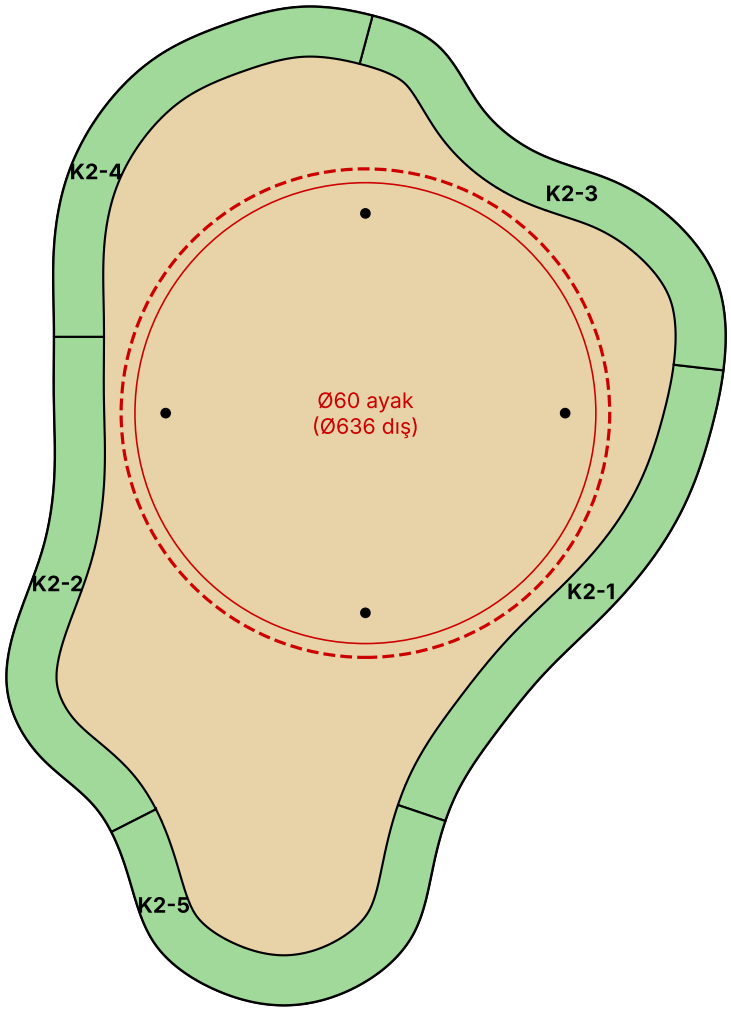


Kesimden sonra şeritlerin üstüne kurşun kalemle K1-1… numarasını yazın (plaka yerleşim sayfasında hangisinin hangisi olduğu var).
1. kat ekleri ile 2. kat ekleri yarım parça kaydırıldı: ekler üst üste gelmez, yolda darbede çatlamaz. Şeritler tabla kenarıyla SIFIR (aynı hizada), tutkal + zımba.
Ayak: 4 adet Ø8 delikten (Ø520 daire, baklava) tablaya vida; tablada Ø3×12 kılavuz delikler hazır. Ayak şeritlere 21 mm mesafede, değmez.

MDF 18 mm — kapaklar + kalınlaştırma

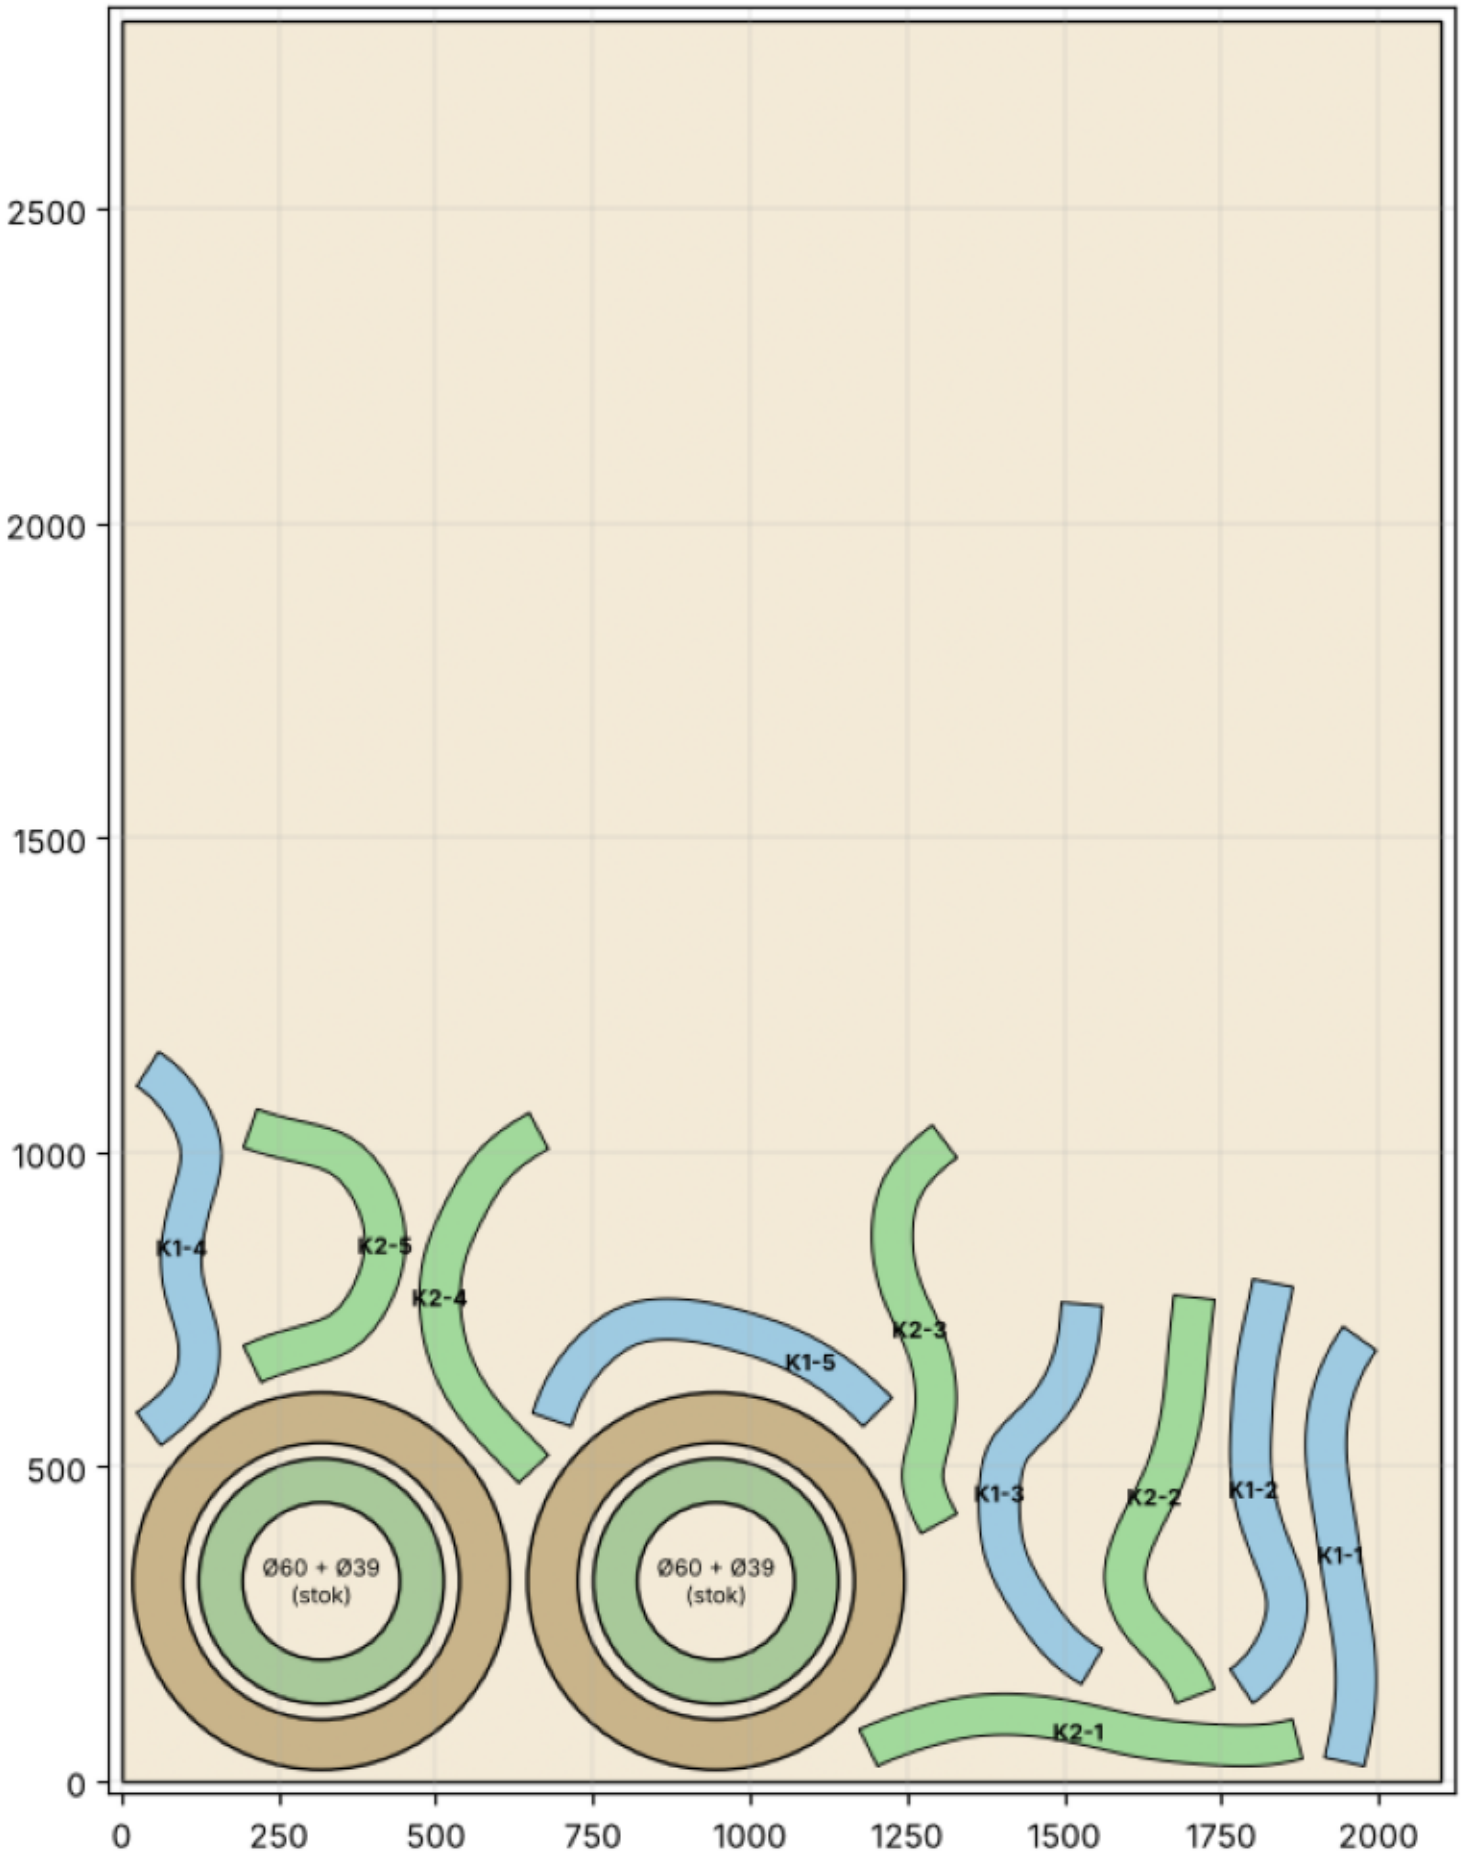

Sıra: Ø8 delikler > Ø39 iç/dış (STOK, 0.2 et) > Ø60 iç > şeritler (küçükten büyüğe, 0.2 et) > Ø60 dış en son.
Ø39 kapaklar Ø60 kapakların boşluğundan bedava çıkar → Ø39 sehpa ayağı için stoğa.

MEŞE KAPLAMA 18 mm — tabla (görünen yüz AŞAĞIDA) + ayak taraması

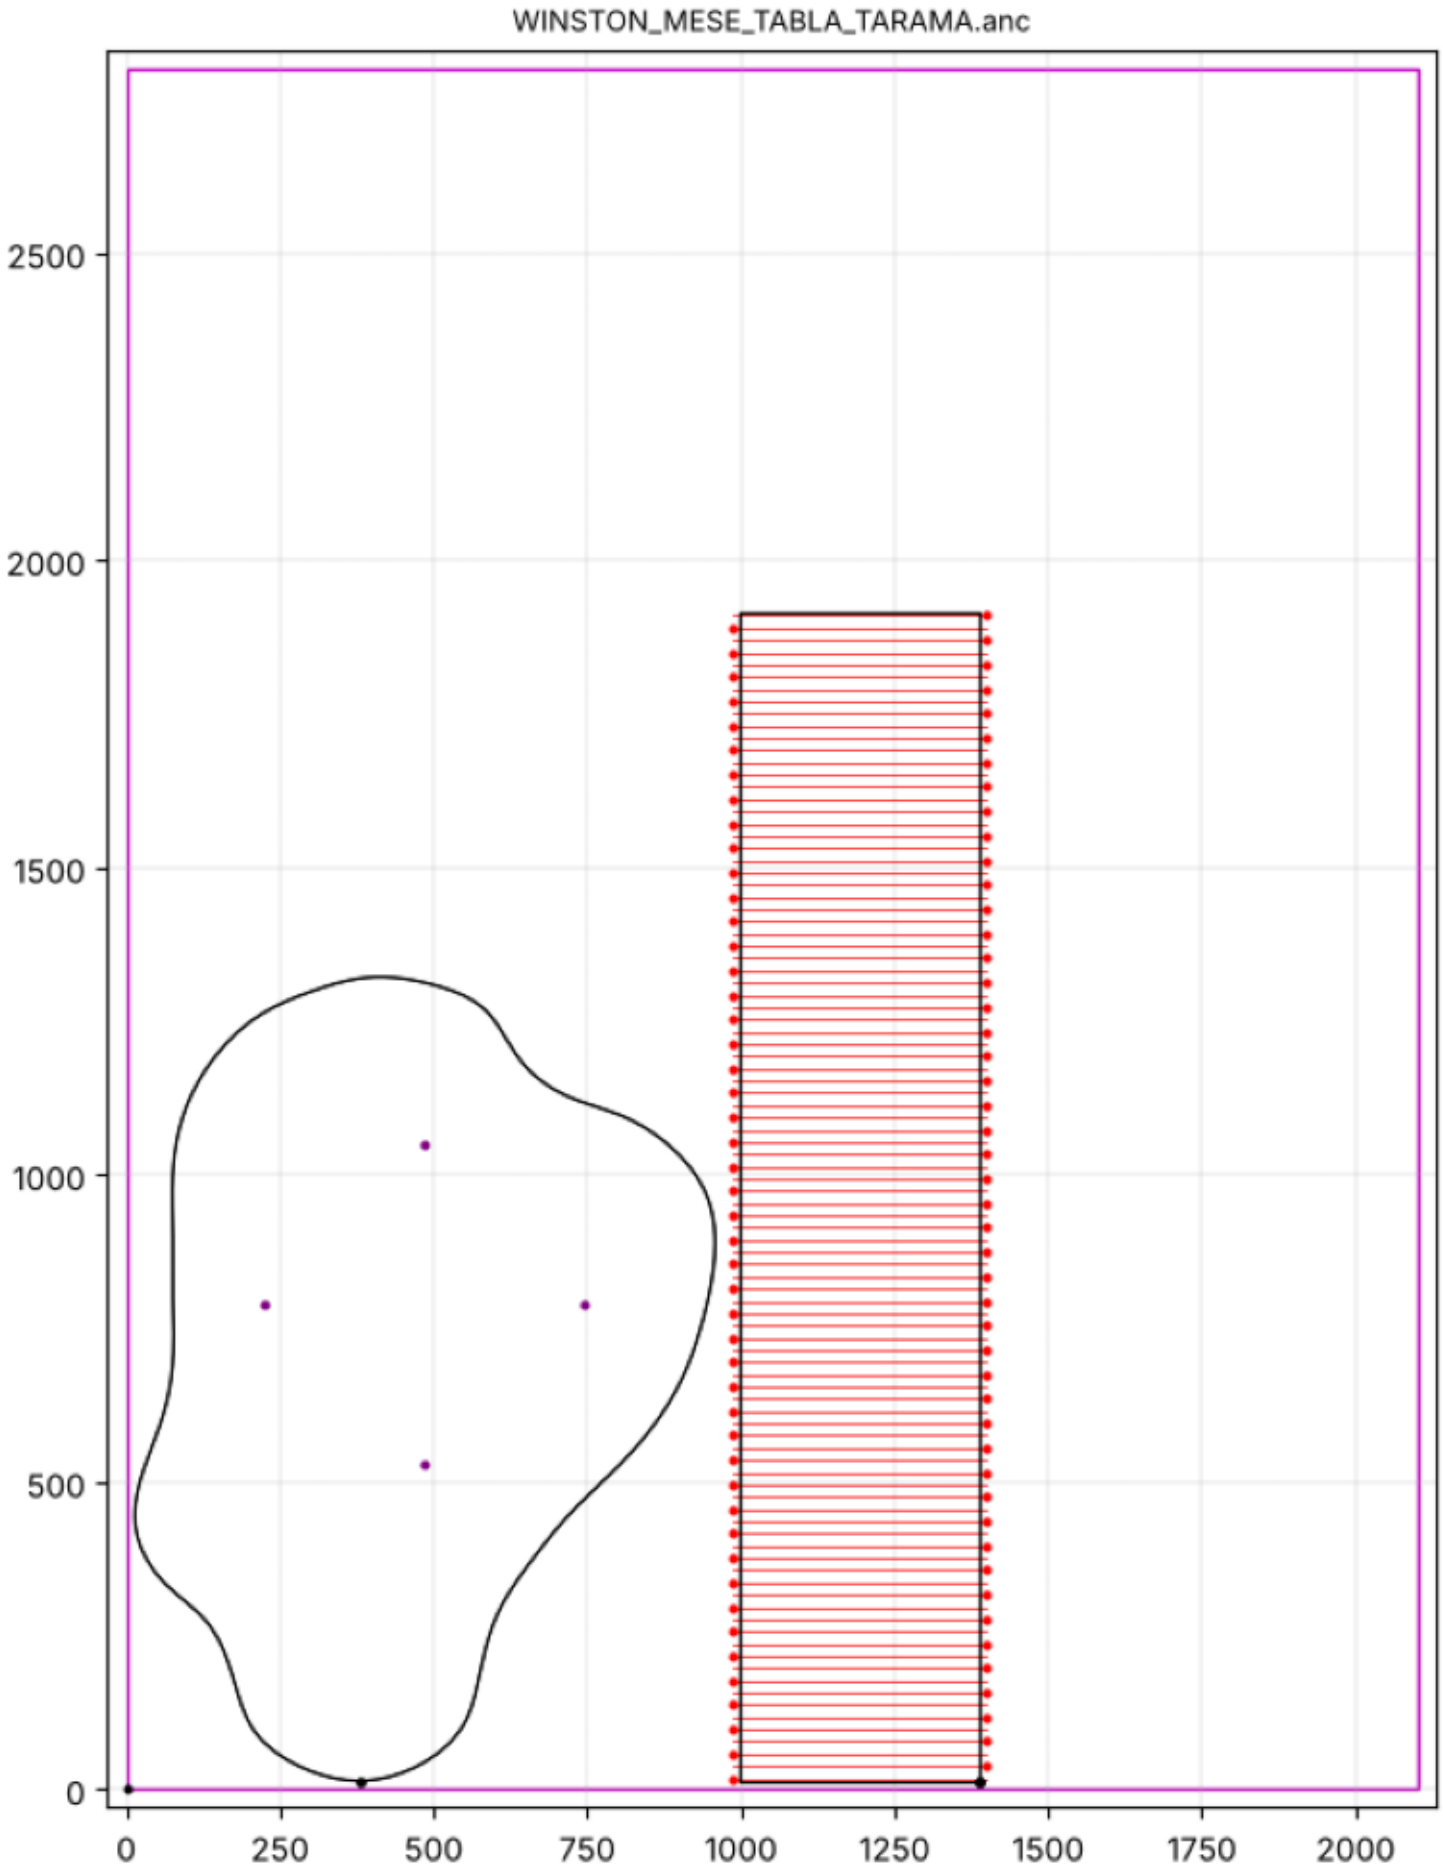

Sıra: T3 Ø3×12 vida kılavuzları > T4 tarama (her oluk ayrı, et 1.1) > T8 tabla (2 paso) > T8 tarama paneli en son (3 paso, F3500).
Tarama paneli 382×1892 DİKİNE yerleştirildi (meşe kaplama su yönü): Ø60 kapak çevresine (π×602.2) göre. Uçlar yarım oluk: ek yeri o

WINSTON ORTA SEHPA — PARÇA LİSTESİ (1 adet sehpa)

MEŞE KAPLAMA 18 mm (WINSTON_MESE_TABLA_TARAMA.anc)
  1 × Tabla, organik form 936 × 1300 mm, altında 4 × Ø3×12 vida kılavuzu
  1 × Ayak tarama paneli 382 × 1892 mm (dikine, su yönünde), 96 oluk (aralık 19.9, 10 mm bıçak, et 1.1)

MDF 18 mm (WINSTON_MDF_KAPAK_KALINLASTIRMA.anc)
  2 × Ø60 ayak kapağı (alt + üst şapka), Ø600 / iç boşluk Ø440, 4 × Ø8 delik (Ø520 daire)
  2 × Ø39 ayak kapağı — STOK (bedava), Ø390 / iç boşluk Ø250, 4 × Ø8 delik (Ø310 daire)
  5 × 1. kat kalınlaştırma şeridi (K1-1 … K1-5), 65 mm
  5 × 2. kat kalınlaştırma şeridi (K2-1 … K2-5), 65 mm

ÖLÇÜLER
  Toplam yükseklik 400 = ayak 382 + tabla 18 · görünen kenar 54 mm
  Ayak dış çapı ≈ Ø636 (Ø600 kapak + 18 mm taramalı panel)
  Tabla çevresi 3514 mm

HIRDAVAT
  4 × vida 4×40 (üst kapak → tabla), keçe 4 adet (alt kapak altına), tutkal + zımba (şeritler)